
План расстановки мебели

4-комнатная квартира · масштаб по обмерному плану · размеры в мм

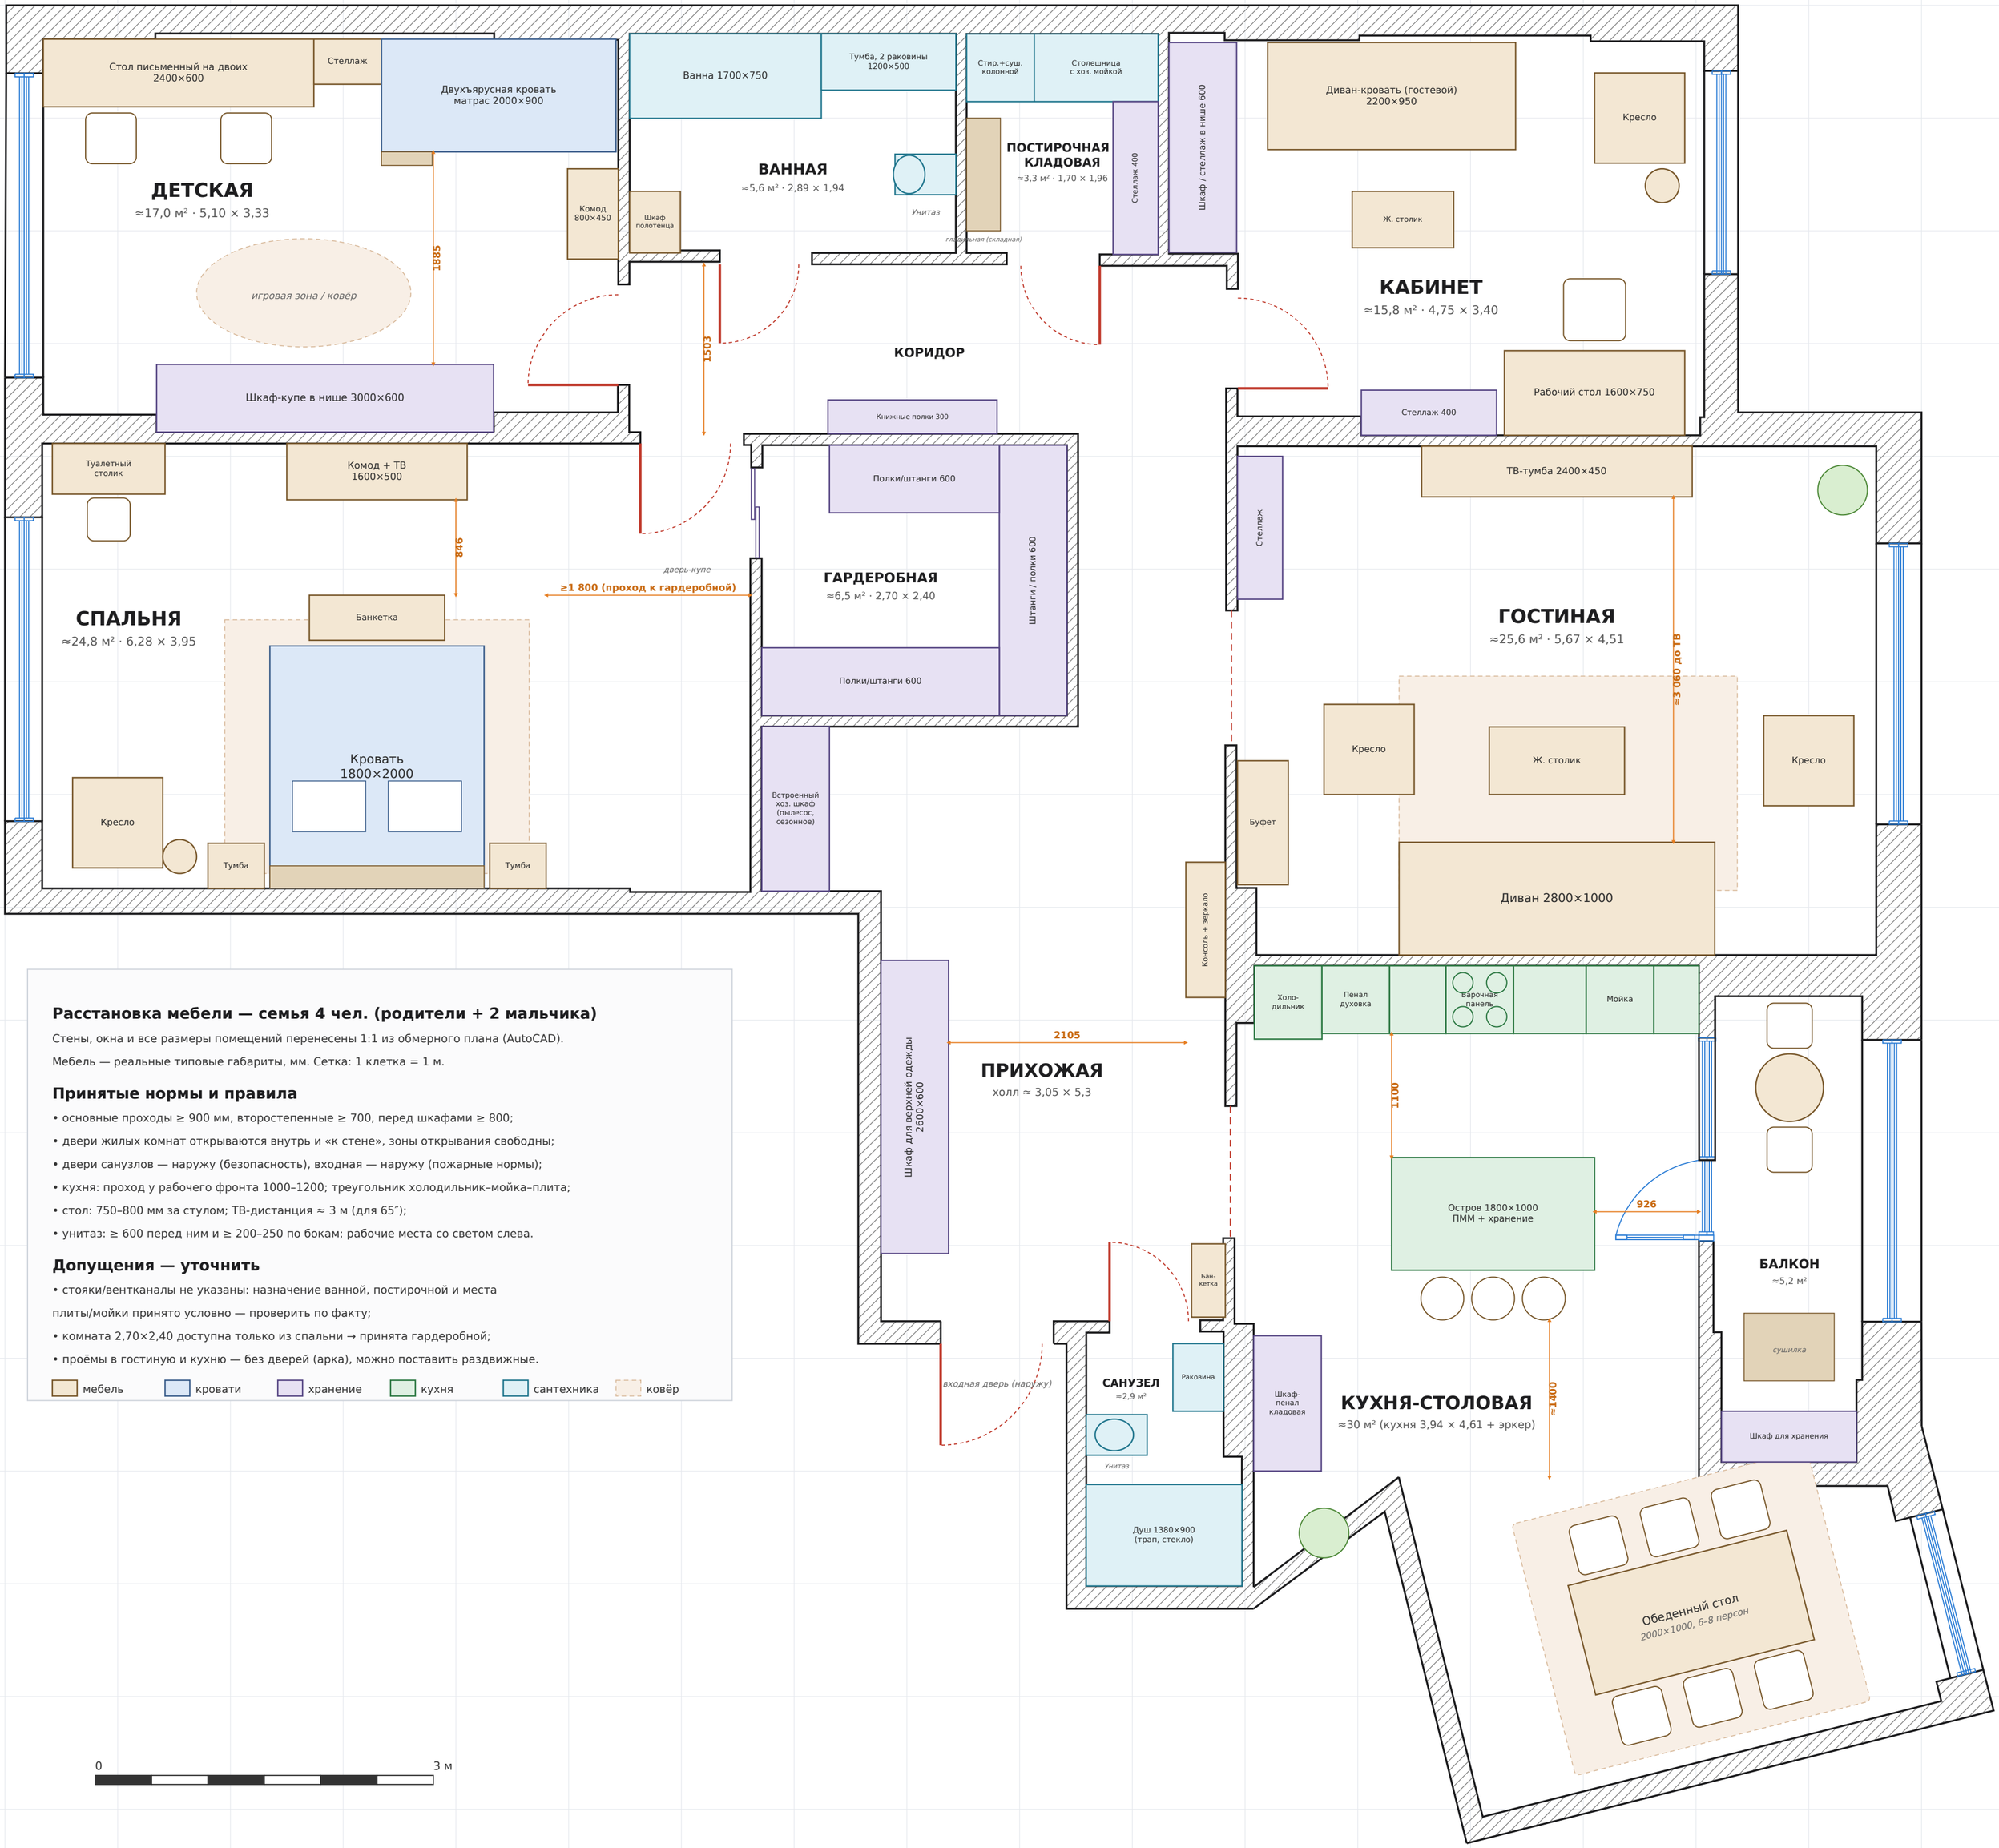

Расстановка мебели — семья 4 чел. (родители + 2 мальчика)

Стены, окна и все размеры помещений перенесены 1:1 из обмерного плана (AutoCAD).

Мебель — реальные типовые габариты, мм. Сетка: 1 клетка = 1 м.

Принятые нормы и правила

- основные проходы ≥ 900 мм, второстепенные ≥ 700, перед шкафами ≥ 800;
- двери жилых комнат открываются внутрь и «к стене», зоны открывания свободны;
- двери санузлов — наружу (безопасность), входная — наружу (пожарные нормы);
- кухня: проход у рабочего фронта 1000–1200; треугольник холодильник–мойка–плита;
- стол: 750–800 мм за стулом; ТВ-дистанция ≈ 3 м (для 65″);
- унитаз: ≥ 600 перед ним и ≥ 200–250 по бокам; рабочие места со светом слева.

Допущения — уточнить

- стояки/вентканалы не указаны: назначение ванной, постирочной и места плиты/мойки принято условно — проверить по факту;
- комната 2,70×2,40 доступна только из спальни → принята гардеробной;
- проёмы в гостиную и кухню — без дверей (арка), можно поставить раздвижные.

мебель · кровати · хранение · кухня · сантехника · ковёр

0 — 3 м